


Important

Report all errors & omission in this drawing to the Team Leader for correction prior to commencement of construction.

LAND AREA = 3.00 KATHA
FLOOR AREA = 1277 SFT
FLOOR AREA = 1532 SFT (WITH COMMON SPACE 20%)

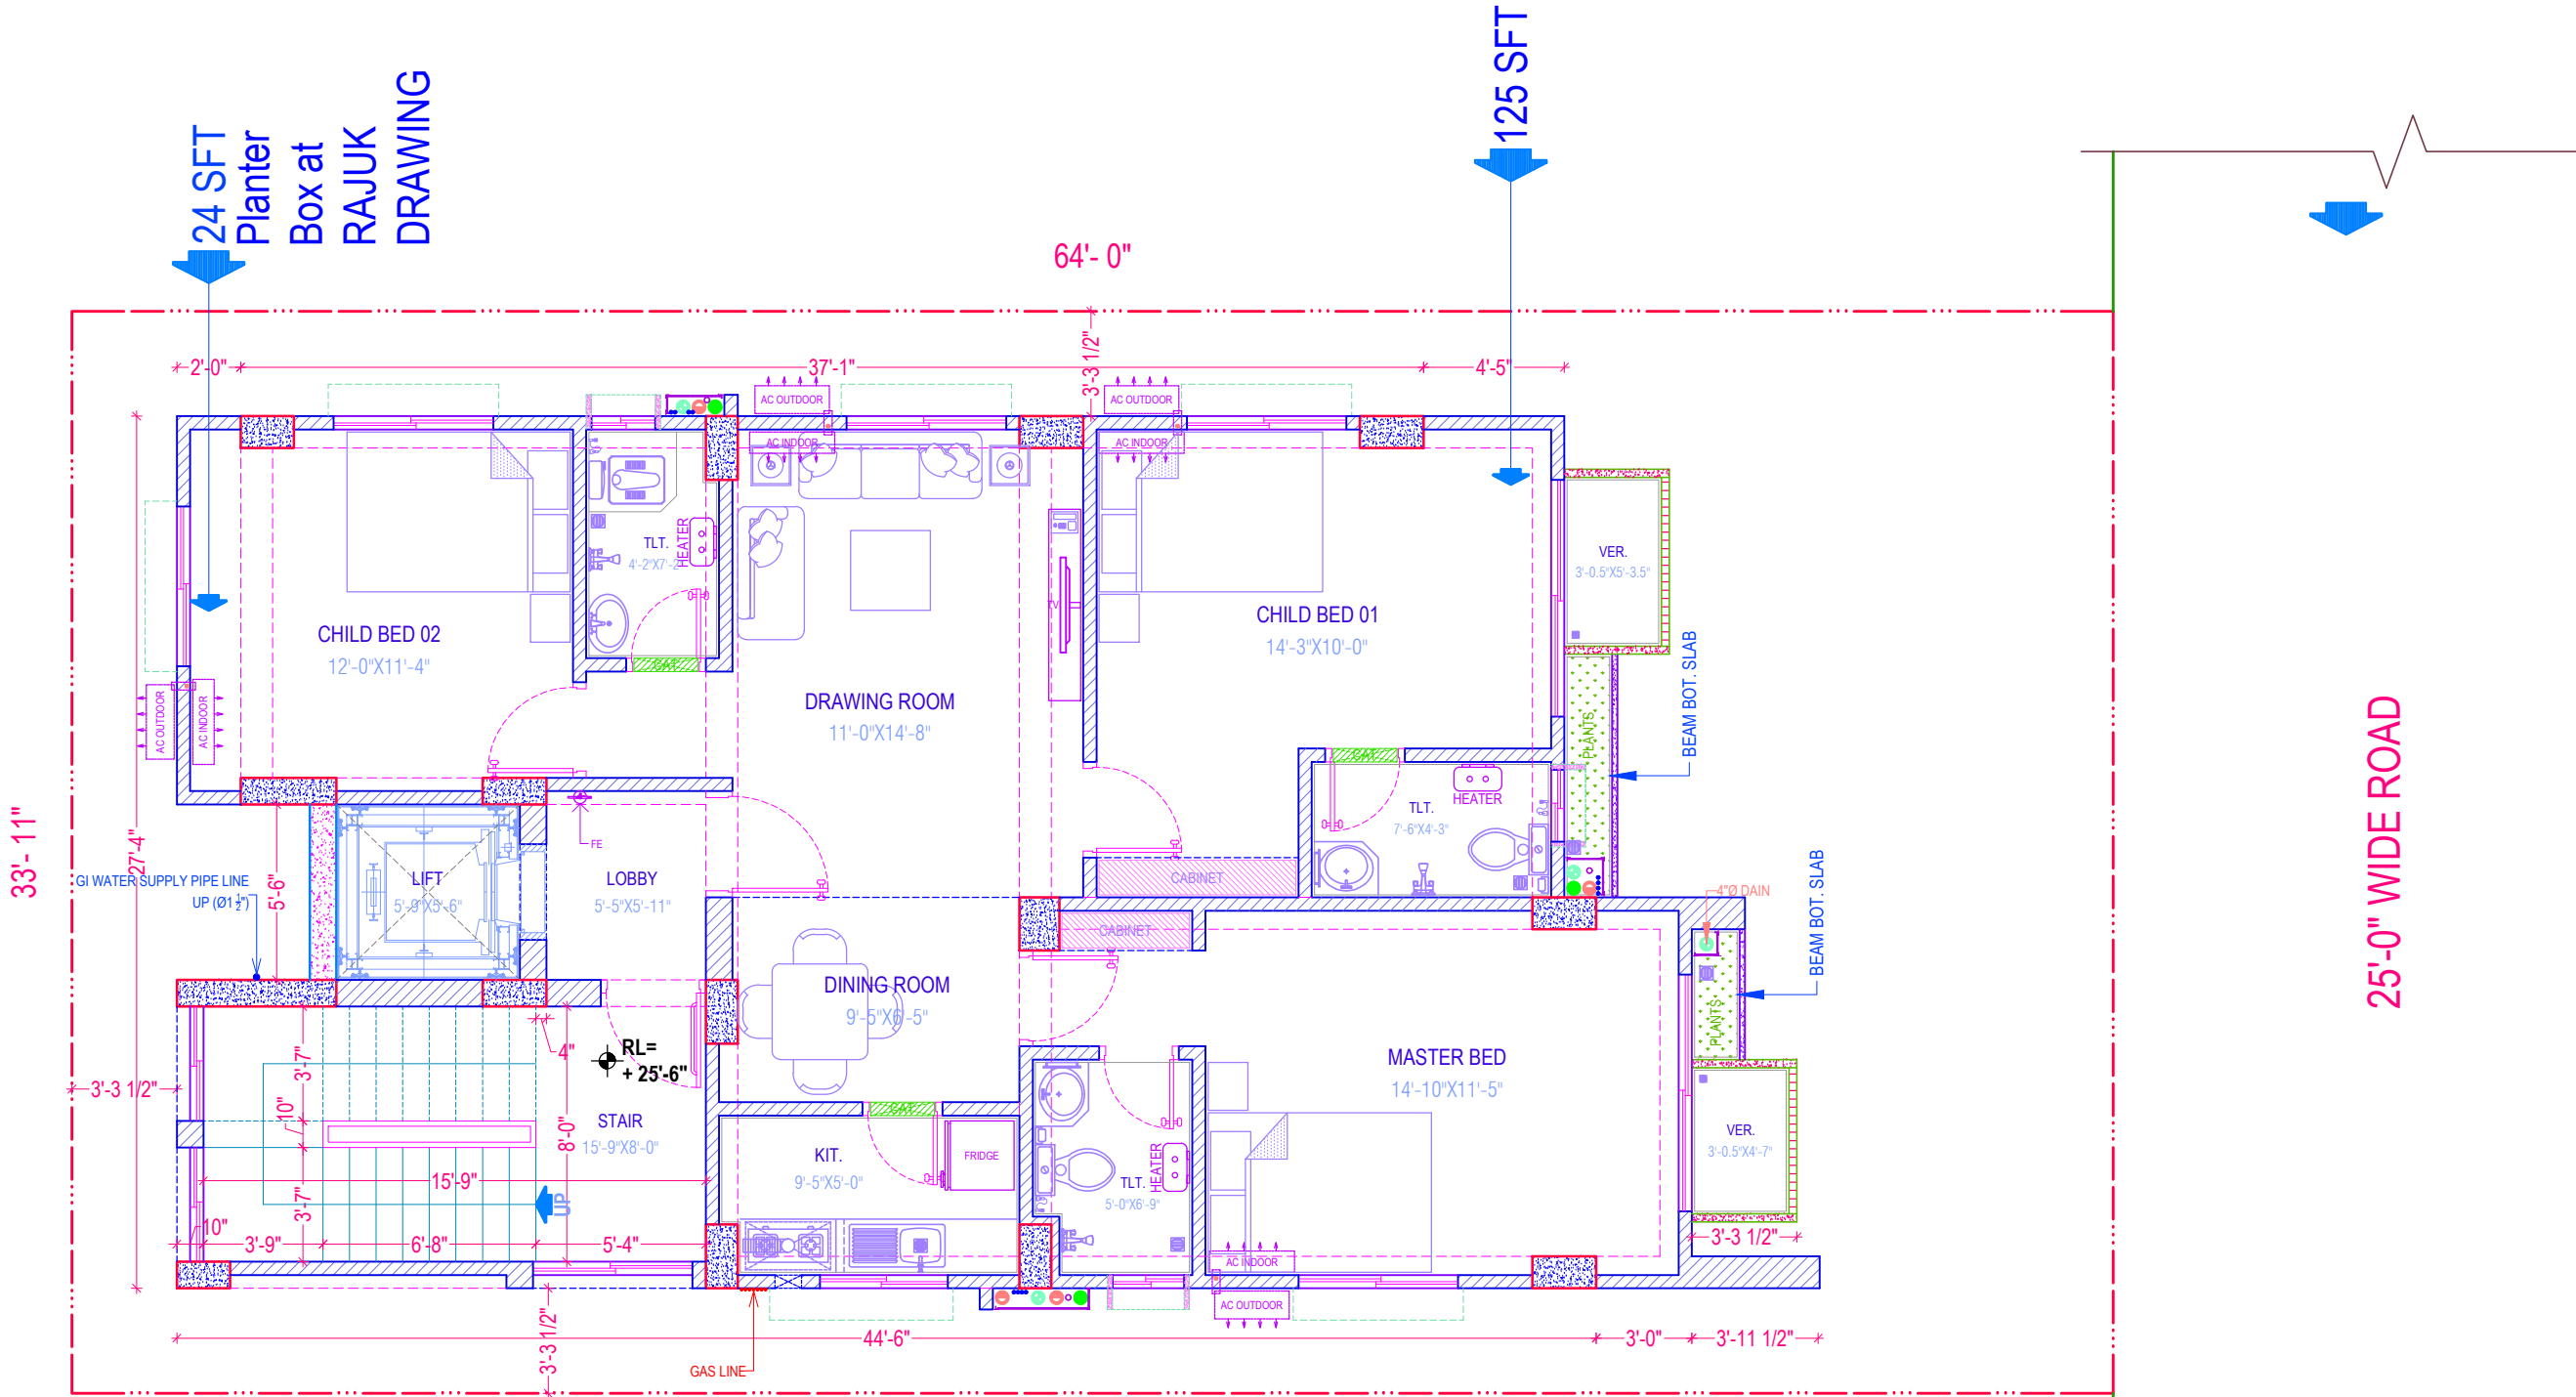

DEVELOPER:
AVENUE CONSTRUCTION LTD.
51, 51/A, RESOURCEFUL PALTAN CITY 7TH FLOOR) PURANA PLATON, DHAKA-1000, BANGLADESH
PROJECT NAME:
AVENUE AHSAN PALACE
NO. OF STOREY:
EIGHT STORIED BUILDING (G+7)
PROJECT ADDRESS:
PLOT NO. 51, BLOCK -E, ROAD NO. 05, BASHUNDHARA, DHAKA-1229, BANGLADESH
PROJECT TYPE:
RESIDENTIAL APARTMENT (A-3)

CONSULTANT:	
DESIGN AIDS & CONSULTANTS LTD. EASTERN PORSHI (3RD FLOOR), HOUSE NO. 74, ROAD NO. 8, BLOCK C, NIKETAN, GULSHAN-1, DHAKA PH: 8836170, CELL PH: 0171 3456 052 email: designaidsdtd@gmail.com	
SIGNATURE:	

TECHNICAL TEAM:	
TEAM LEADER :	ENGR. MARUF AHMED IEB MEMBERSHIP NO. F-09092, DMINB/CE-0123, DCB E-131 REGISTERED STRUCTURAL ENGINEER, ECPS
ARCHITECT :	SHARMIN AFROZ SHUMI IAB MEMBERSHIP & REG. S-104 MD. MOMINUL ISLAM MEMBERSHIP & REG. I-048
STRUCTURAL ENGINEER :	ENGR. MD. MATIUR RAHMAN IEB MEMBERSHIP NO. F-7628 RAJUK REG. NO. DMINB/CE-0316 ENGR. MD. HUMAYUN KABIR IEB MEMBERSHIP NO. M-21732 RAJUK REG. NO. DMINB/CE-0075
PLUMBING ENGINEER :	ENGR. MD. TASFIQUR RAHMAN IEB MEMBERSHIP NO. M-18376
ELECTRICAL ENGINEER :	ENGR. MD. ABDUL MOMEN
MECHANICAL ENGINEER :	ENGR. MUHAMMAD AKHTERUZZAMAN IEB MEMBERSHIP NO. F-12973
CAD BY:	MD. TUTUL HOSSAIN

NOTES
ALL CONTRACTORS MUST CHECK ALL DIMENSIONS ON SITE. ONLY FIGURED DIMENSIONS AND GRID LINES ARE TO BE WORKED OUT. ANY DISCREPANCIES FROM THAT MUST BE REPORTED TO THE ENGINEERS CONCERNED BEFORE PROCESSING.
COPYRIGHT
IT'S A PRODUCTION OF DESIGN AIDS & CONSULTANTS LTD. THIS DESIGN IS EXCLUSIVELY COPYRIGHTED. THESE DRAWINGS & DESIGN, OR PARTS THERE OF, CAN NOT BE COPIED OR REPRODUCED OR USED IN ANY FORM WITHOUT THE PRIOR PERMISSION OF THE ORGANIZATION.

REMARKS :

DRAWING TITLE :
TYPICAL FLOOR PLAN
SCALE :
1" = 6'-0"

DIRECTION:	SHEET NO:
	A-03